


Погоджено:		
Інв. N ориг.	Взам. інв. №	
	Підпис і дата	

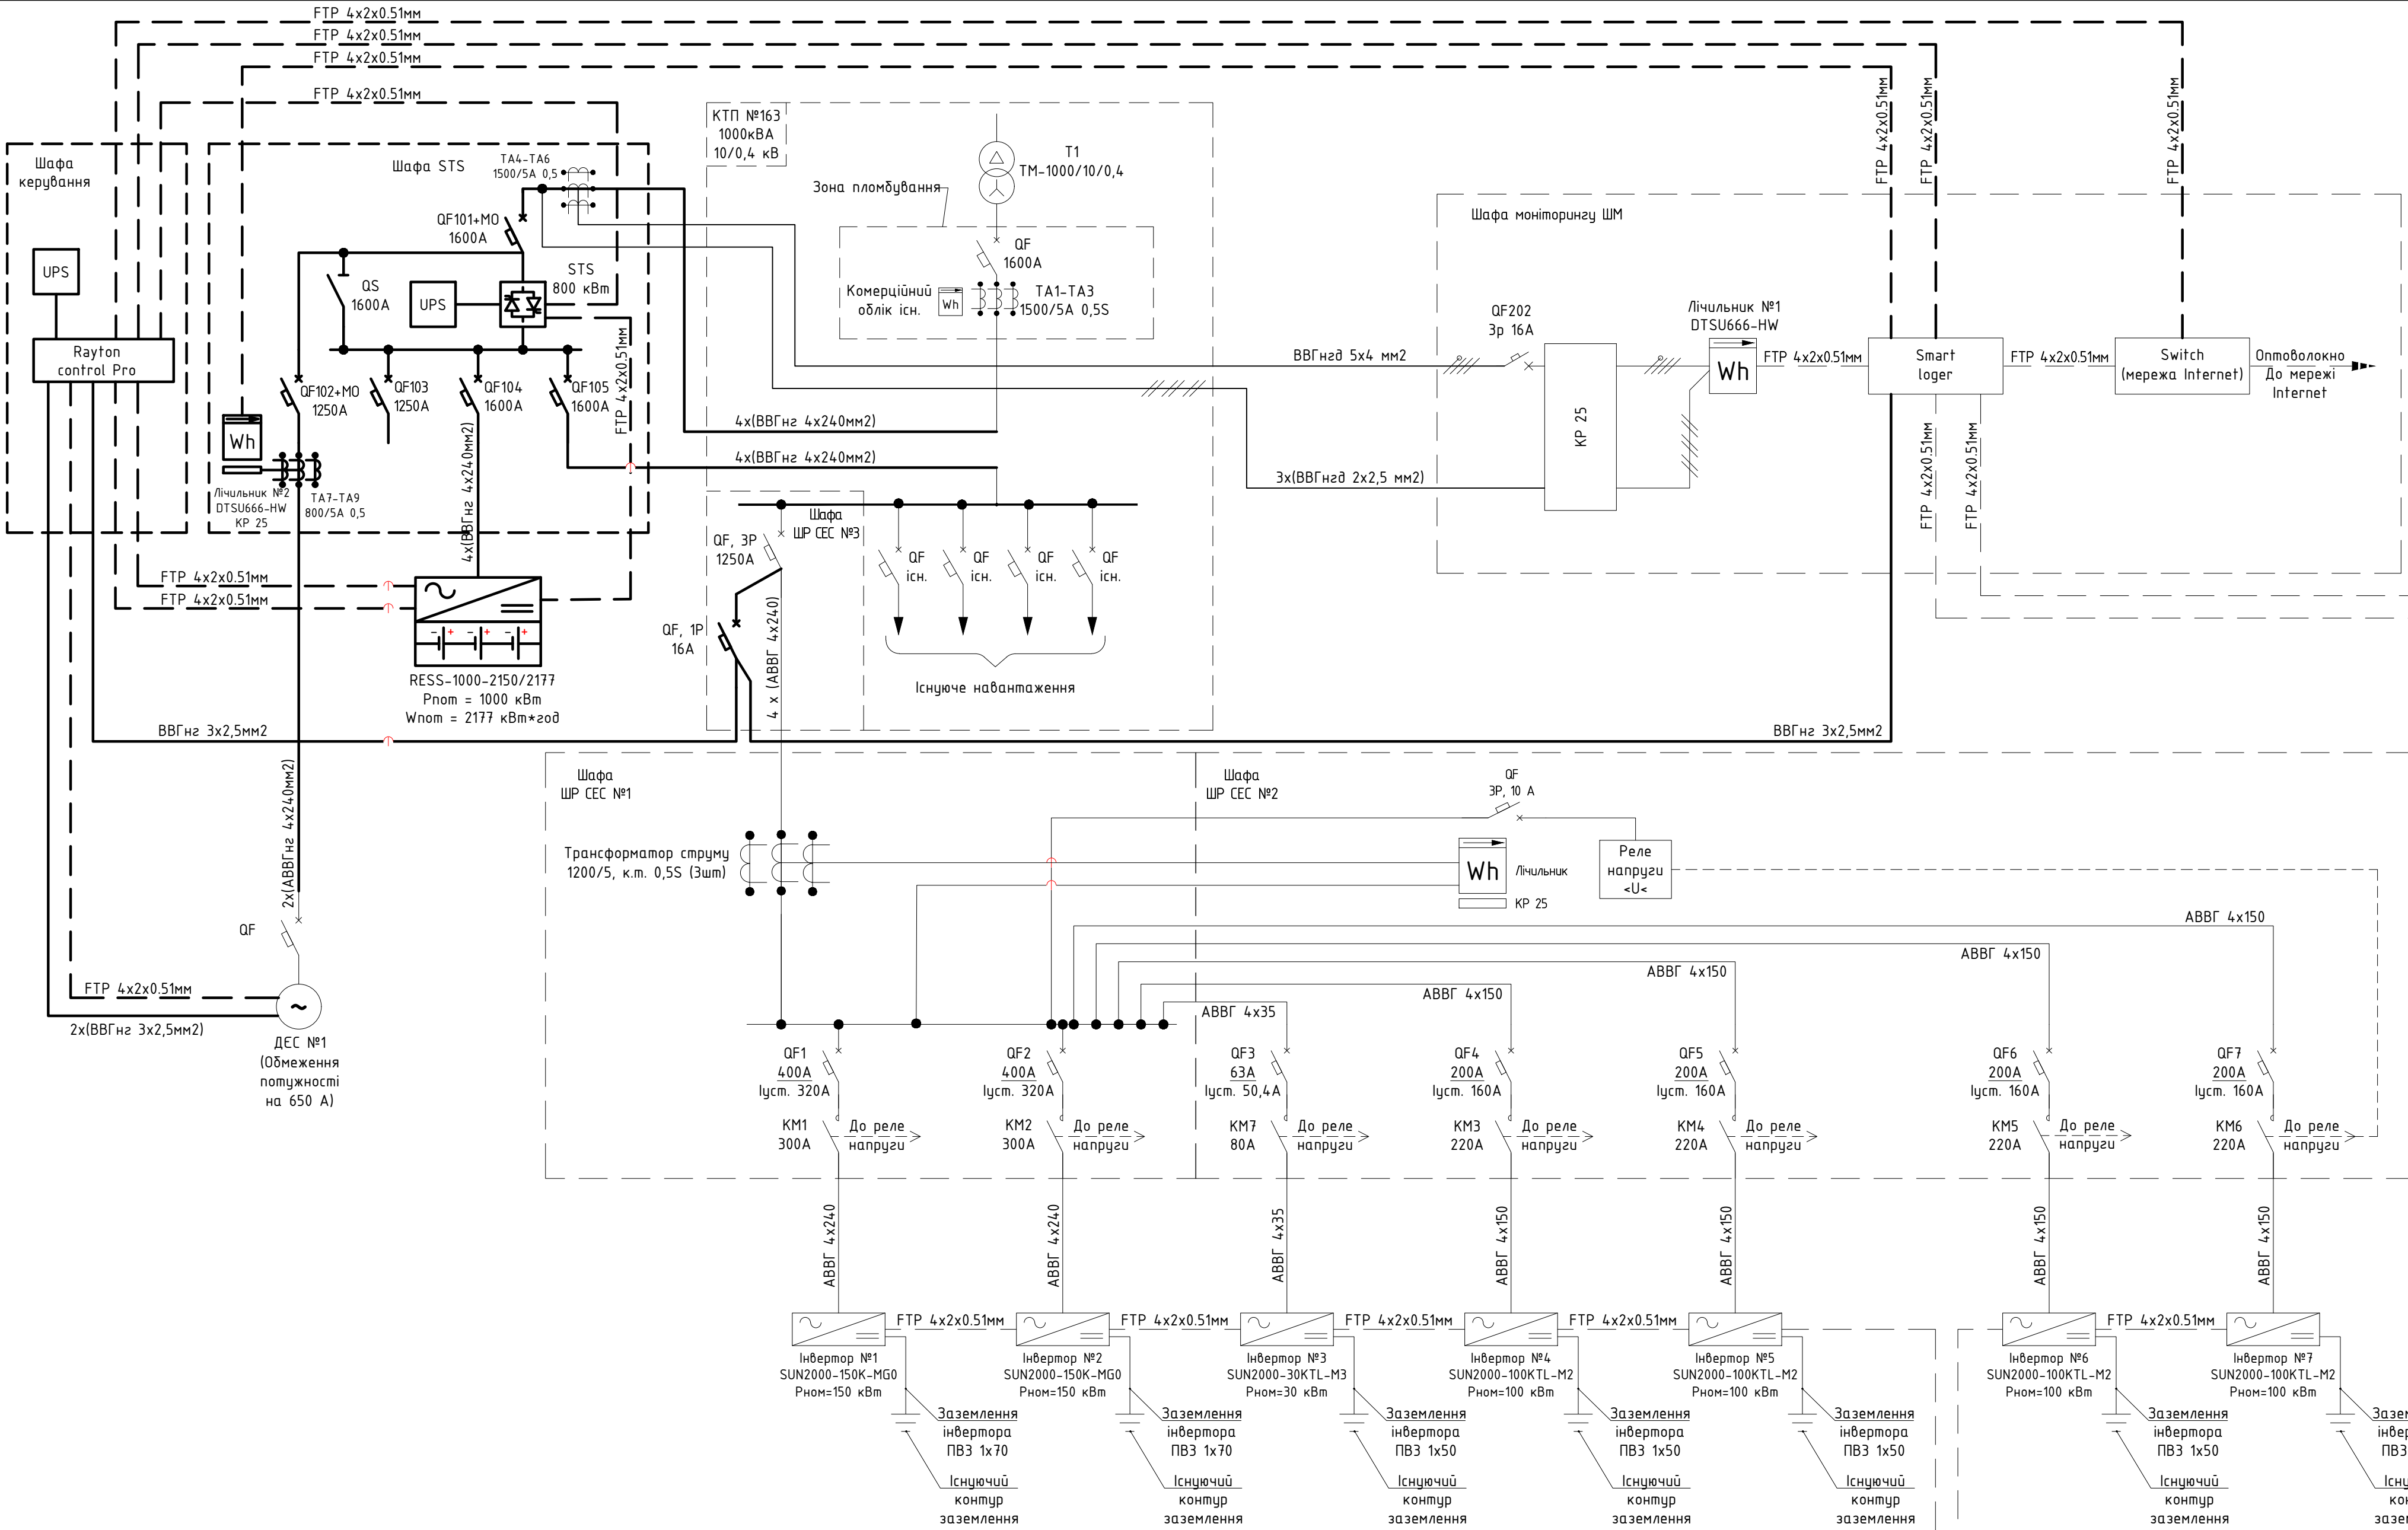

Примітки:
1. Потовщеною лінією показано проектоване обладнання, тонкою - існуюче.

						23225-01-ETP			
						Реконструкція системи електропостачання ТОВ «ФАКТОРІЯ-АГРО» з встановленням установки зберігання енергії за адресою: Київська обл., м. Вишгород, вул. Новопромислова, д. 1			
Зм.	Кільк.	Арк.	№ док.	Підпис	Дата	Електротехнічні рішення	Стадія	Аркуш	Аркушів
ГІП		Новік О.М.		<i>Новік</i>	08.25		РП	2	
						Схема електрична принципова підключення УЗЕ	RAYTON SOLAR MADE EASY		
Розробив		Новік О.М.		<i>Новік</i>	08.25				